
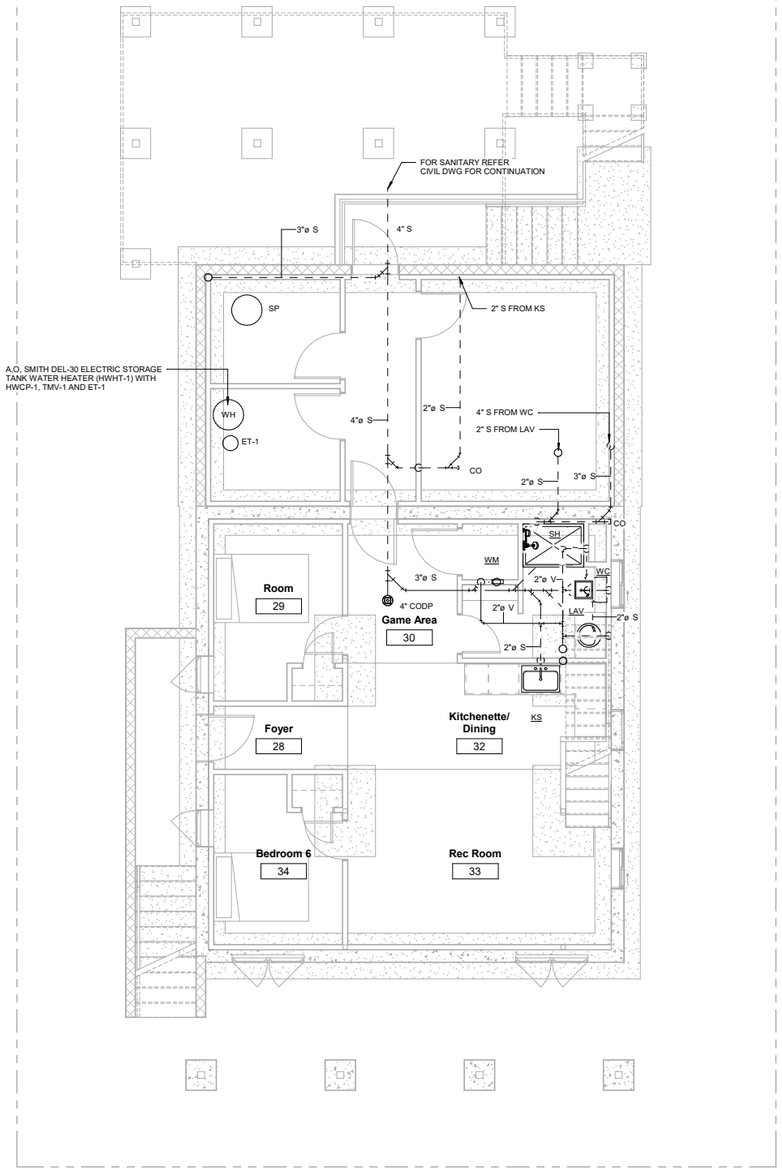


1 Basement
1/4" = 1'-0"

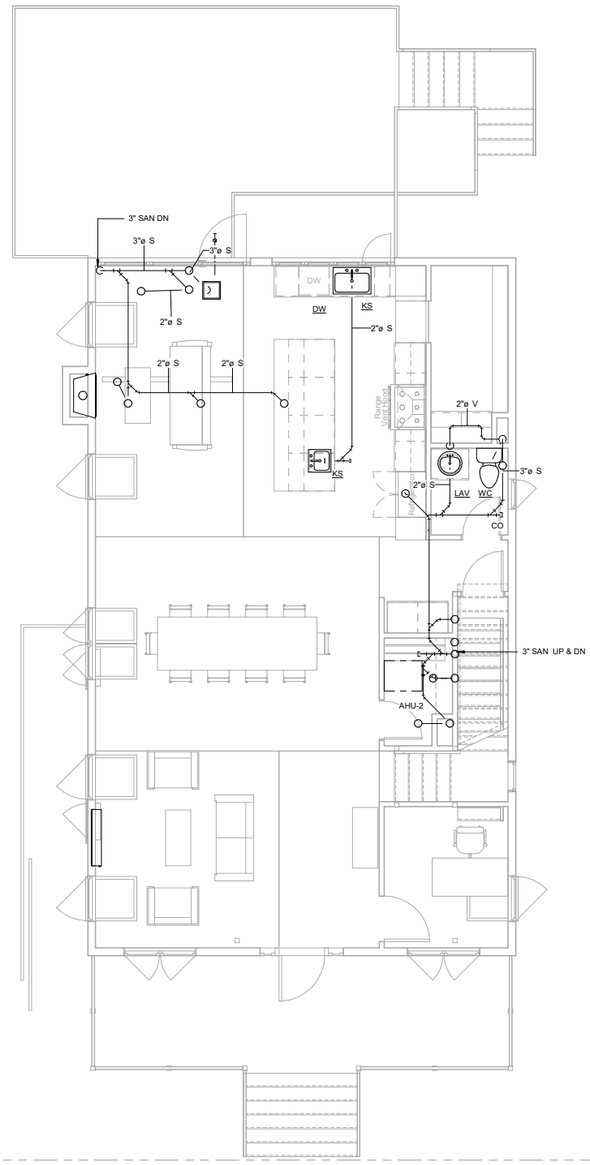

2 First Floor
1/4" = 1'-0"

ARCOS DESIGN
4500 New Hampshire Avenue NW
Washington, DC 20011
202.780.5599 | 646.678.6348


Project
4518 9th Street NW Remodel
4518 9th Street NW
Washington, DC 20011

Issue


Drawn by:	KS	Project No.	A2217
Checked by:	KS	Scale:	1/4" = 1'-0"

Sheet Name
BASEMENT AND FIRST FLOOR PLAN-SANITARY

P101
Sheet Number

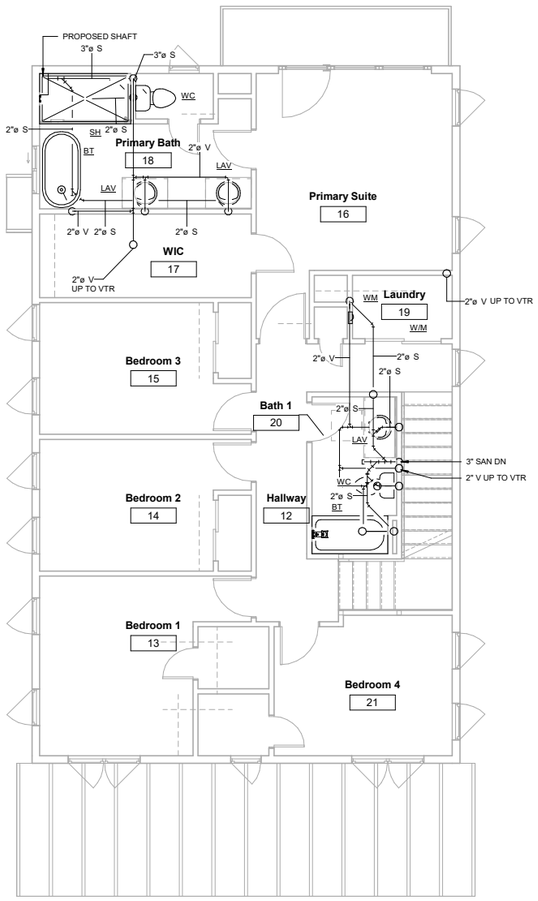

1 Second Floor
1/4" = 1'-0"

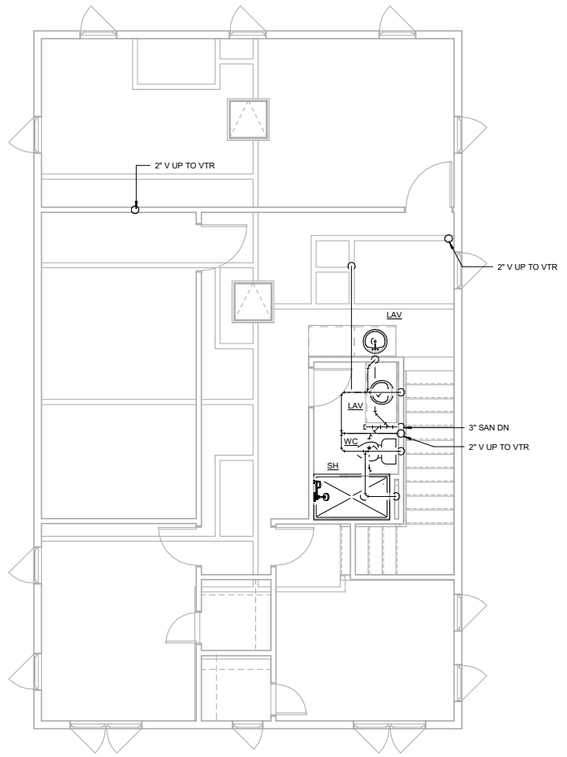

2 Third Floor
1/4" = 1'-0"

ARCOS DESIGN
4500 New Hampshire Avenue NW
Washington, DC 20011
202.780.5599 | 646.678.6348


Project
4518 9th Street NW Remodel
4518 9th Street NW
Washington, DC 20011

Issue


Drawn by:	KS	Project No.	A2217
Checked by:	KS	Scale:	1/4" = 1'-0"

Sheet Name
SECOND AND THIRD FLOOR PLAN - SANITARY

P102
Sheet Number

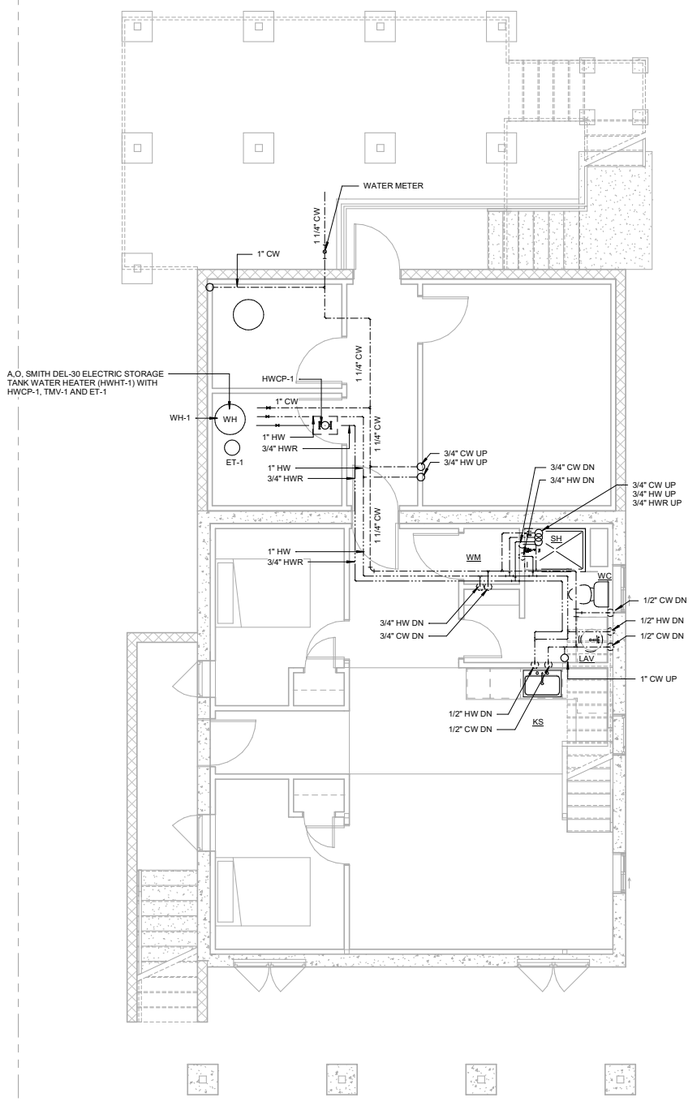

1 Basement Copy 3
1/4" = 1'-0"

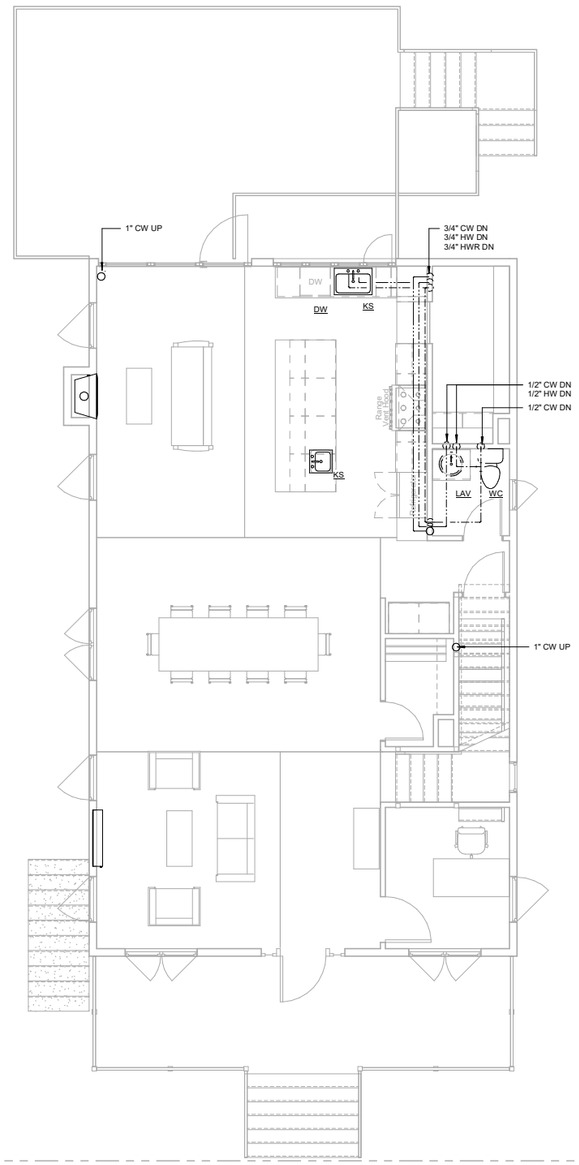

2 First Floor Copy 2
1/4" = 1'-0"

ARCOS DESIGN
4500 New Hampshire Avenue NW
Washington, DC 20011
202.780.5599 | 646.678.6348

Project

4518 9th Street NW Remodel

4518 9th Street NW
Washington, DC 20011

Issue


Drawn by:	KS	Project No.	A2217
Checked by:	KS	Scale:	1/4" = 1'-0"

Sheet Name


BASEMENT AND FIRST FLOOR PLAN-WATER SUPPLY

P103

Sheet Number

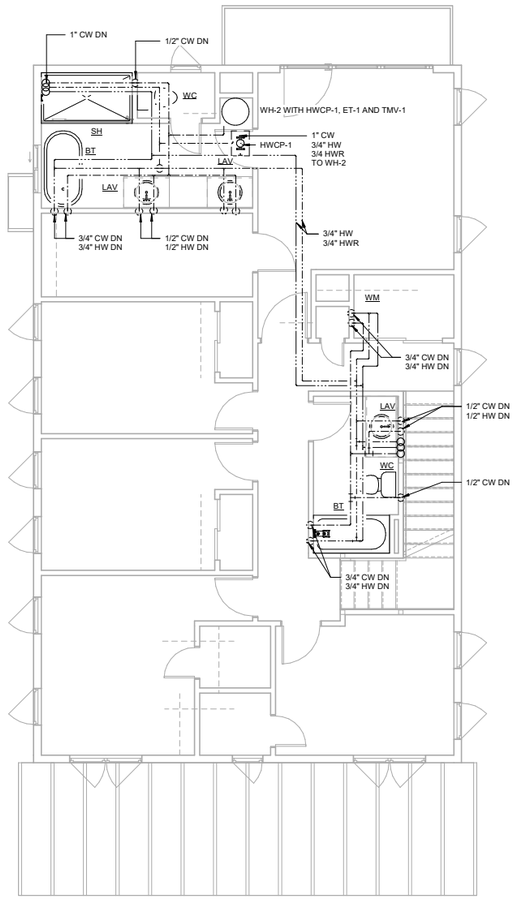

1 Second Floor Copy 2
1/4" = 1'-0"

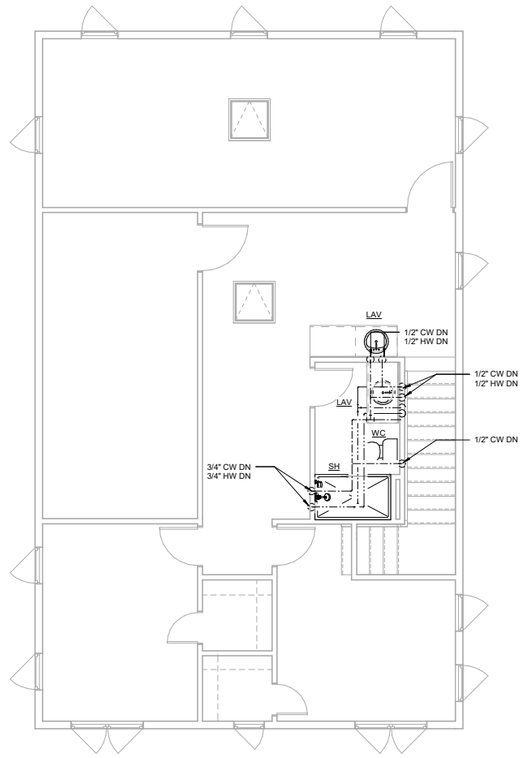

2 Third Floor Copy 2
1/4" = 1'-0"

ARCOS DESIGN
4500 New Hampshire Avenue NW
Washington, DC 20011
202.780.5599 | 646.678.6348

Project

4518 9th Street NW Remodel

4518 9th Street NW
Washington, DC 20011

Issue


Drawn by:	KS	Project No.	A2217
Checked by:	KS	Scale:	1/4" = 1'-0"

Sheet Name

SECOND AND THIRD FLOOR PLAN - WATER SUPPLY

P104

Sheet Number

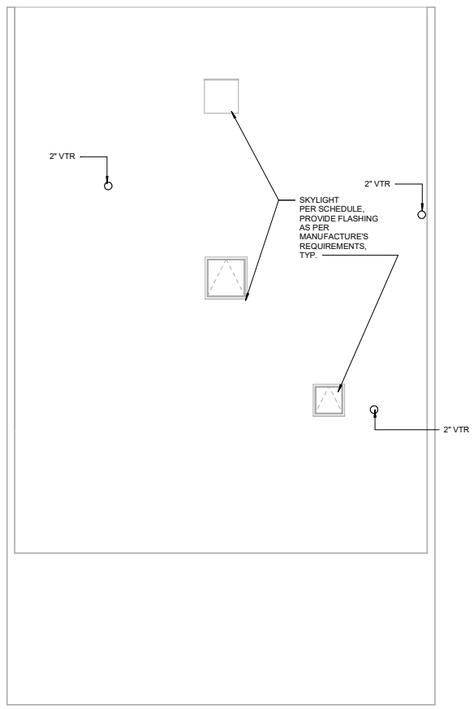

1 Roof Plan
1/4" = 1'-0"

ARCOS DESIGN
4500 New Hampshire Avenue NW
Washington, DC 20011
202.780.5599 | 646.678.6348

Project

4518 9th Street NW Remodel

4518 9th Street NW
Washington, DC 20011

Issue

Drawn by:	KS	Project No.	A2217
Checked by:	KS	Scale:	1/4" = 1'-0"

Sheet Name

ROOF PLUMBING PLAN

P105

Sheet Number

ELECTRIC WATER HEATER (STORAGE BTANK TYPE)										
ITEM NUMBER	FIXTURW DESCRIPTION	DIMENSIONS	MAX INPUT KW	UNIORM ENERGY FACTOR	STORAGE WATER TEMP	STOR. CAP. (GAL)	RECOVERY CAP. (GAL)	TYPE	ELECT. CHARACERISTIC CONTROLS	MANUFACTURER & MODEL NO.
WH -1	WATER HEATER	26"D X 33"H	9	0.92	140	30	36	ELECTRIC STORAGE TYPE WATER HEATER	120V/1/60HZ	A.O. SMITH DEL-30
WH -2	WATER HEATER	23"D X 32"H	12	0.92	140	40	49	ELECTRIC STORAGE TYPE WATER HEATER	120V/1/60HZ	A.O. SMITH DEL-40

RECIRCULATION PUMP SCHEDULE

ITEM NUMBER	FIXTURE DESCRIPTION	INLET	FLOW (GPM)	HEAD (FT)	ELECTRIC V/P	WEIGHT (lb)	MANUFACTURER	MODEL	MOTOR RPM	REMARK
RCP	RECIRCULATION PUMP	1/2"	2	7	115/1	9	BELL & GOSSETT	NBF-8S/LW	2800	-

SUMP PUMP SCHEDULE

ITEM NUMBER	FIXTURE DESCRIPTION	CAPACITY (GPM)	HORSEPOWER	DISCHARGE (INCH)	ELECTRIC V/P	HEAD (FEET)	MANUFACTURER	MODEL	REMARK
SP	SUMP PUMP	53	0.4	4	115/1	10	ZOELLER	N152	-

EXPANSION TANK SCHEDULE						
ITEM NUMBER	FIXTURW DESCRIPTION	DIMENSIONS	QUANTITY	LOCATION	GALLONS	MANUF. & MODEL
ET-1	EXPANSION TANK	8"D X 13"H	2	REFER PLAN	2	AMTROL ST-5

MASTER THERMOSTATIC MIXING VALVE											
ITEM NUMBER	FIXTURW DESCRIPTION	QUANTITY	LOCATION	SERVICE	MANUF. & MODEL	CAPACITY (GPM)	PRESSURE DROP	MINIMUM FLOW (GPM)	CW INLET	HIGH TEMP. INLET	LOW TEMP. INLET
TMV-1	THERMOSTATIC MIXING VALVE	2	REFER PLAN	HOT WATER	ACORN MV17-2	15	5	0.5	3/4"	3/4" (140°F)	1" (110°F)

PLUMBING FIXTURE SCHEDULE

ITEM NUMBER	FIXTURE DESCRIPTION	MINIMUM FIXTURE CONNECTION PIPE SIZE				MOUNTING	REMARK
		WASTE	VENT	COLD WATER	HOT WATER		
LAV	LAVATORY	1-1/2"	1-1/2"	1/2"	1/2"	WALL	
WC	WATER CLOSET	3"	1-1/2"	1/2"	-	FLOOR	
SH	SHOWER	2"	1-1/2"	1/2"	1/2"	FLOOR	
WM	WASHING MACHINE	2"	1-1/2"	1/2"	1/2"	FLOOR	
TUB	BATHTUB	2"	1-1/2"	1/2"	1/2"	FLOOR	

SCHEDULE NOTE :

1. MINIMUM PIPE SIZE OF UNDERGROUND PIPING SHALL BE 2".
   - ALL FIXTURES SHALL BE APPROVED BY OWNER/ARCHITECT.

ARCOSDESIGN
4500 New Hampshire Avenue NW
Washington, DC 20011
202.780.5599 | 646.678.6348

Project

4518 9th Street NW Remodel

4518 9th Street NW
Washington, DC 20011

Issue


Drawn by:	KS	Project No.	A2217
Checked by:	KS	Scale:	1" = 1'-0"

Sheet Name


PLUMBING SCHEDULES

P106

Sheet Number

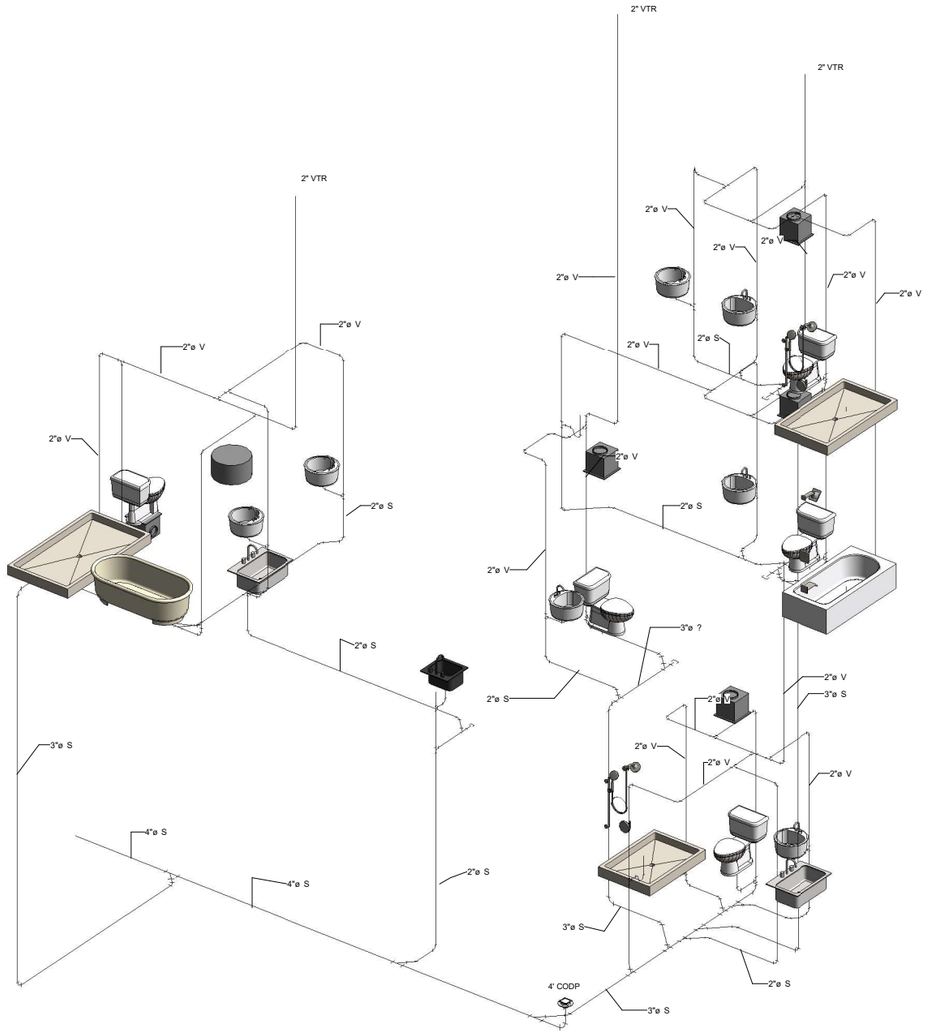

1 3d view sanitary

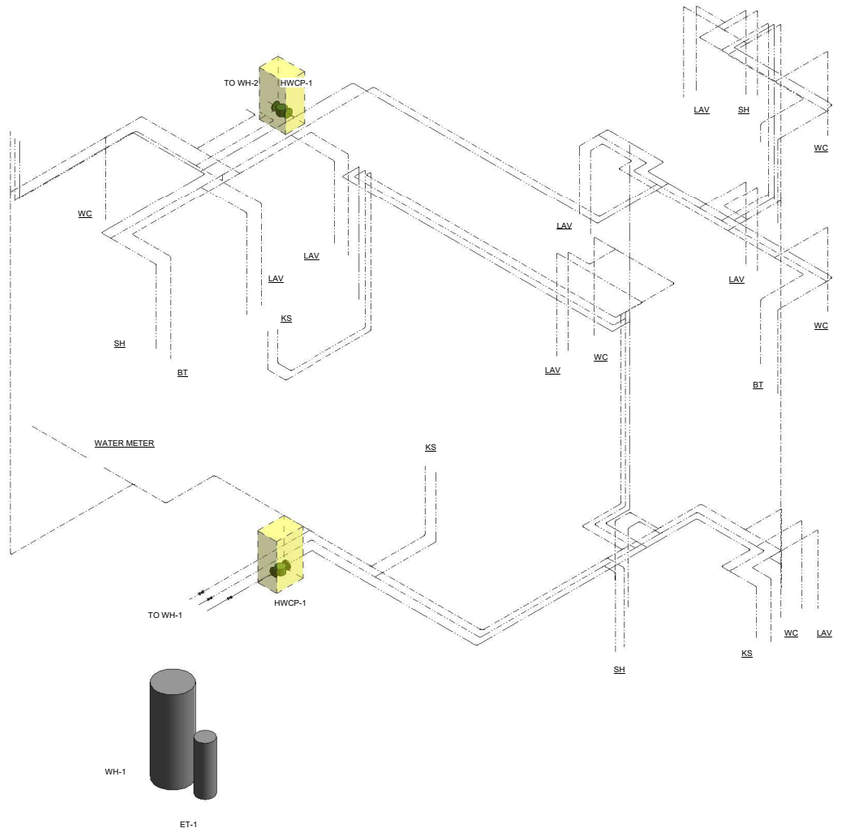

2 3d view water supply

ARCOS DESIGN
4500 New Hampshire Avenue NW
Washington, DC 20011
202.780.5599 | 646.678.6348

Project

4518 9th Street NW Remodel

4518 9th Street NW
Washington, DC 20011

Issue

Drawn by:	KS	Project No.	A2217
Checked by:	KS	Scale:	

Sheet Name

PLUMBING ISOMETRIC VIEWS

P109

Sheet Number