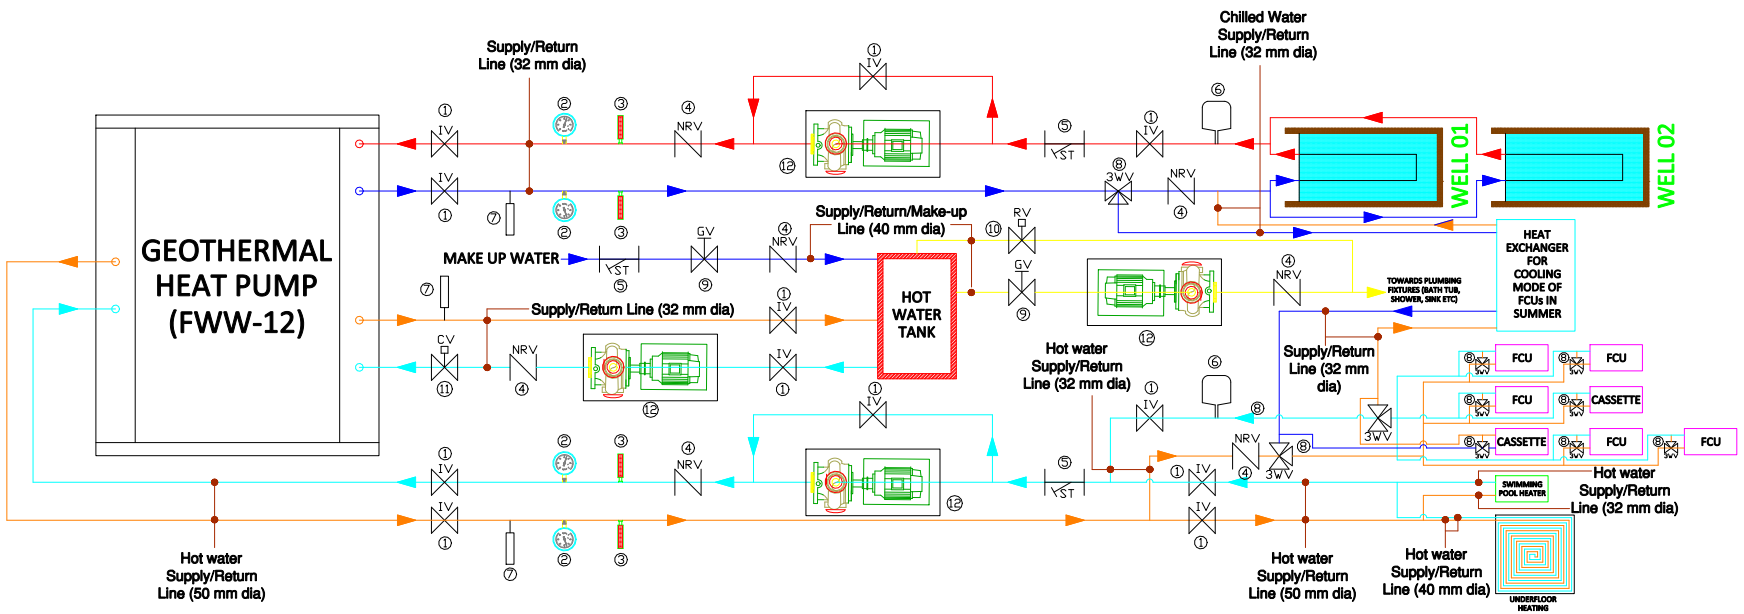


LEGENDS:

①	IV	ISOLATION VALVE
②		PRESSURE GAUGE
③		TEMPERATURE GAUGE
④	NRV	NON RETURN VALVE/CHECK VALVE
⑤	YST	STRAINER
⑥		EXPANSION TANK
⑦		FLOW SWITCH
⑧	3WV	3-WAY VALVE
⑨	GV	GATE VALVE
⑩	RV	RETURN VALVE
⑪	CV	CIRCULATING VALVE
⑫		PUMP

SCHEMATIC DIAGRAM