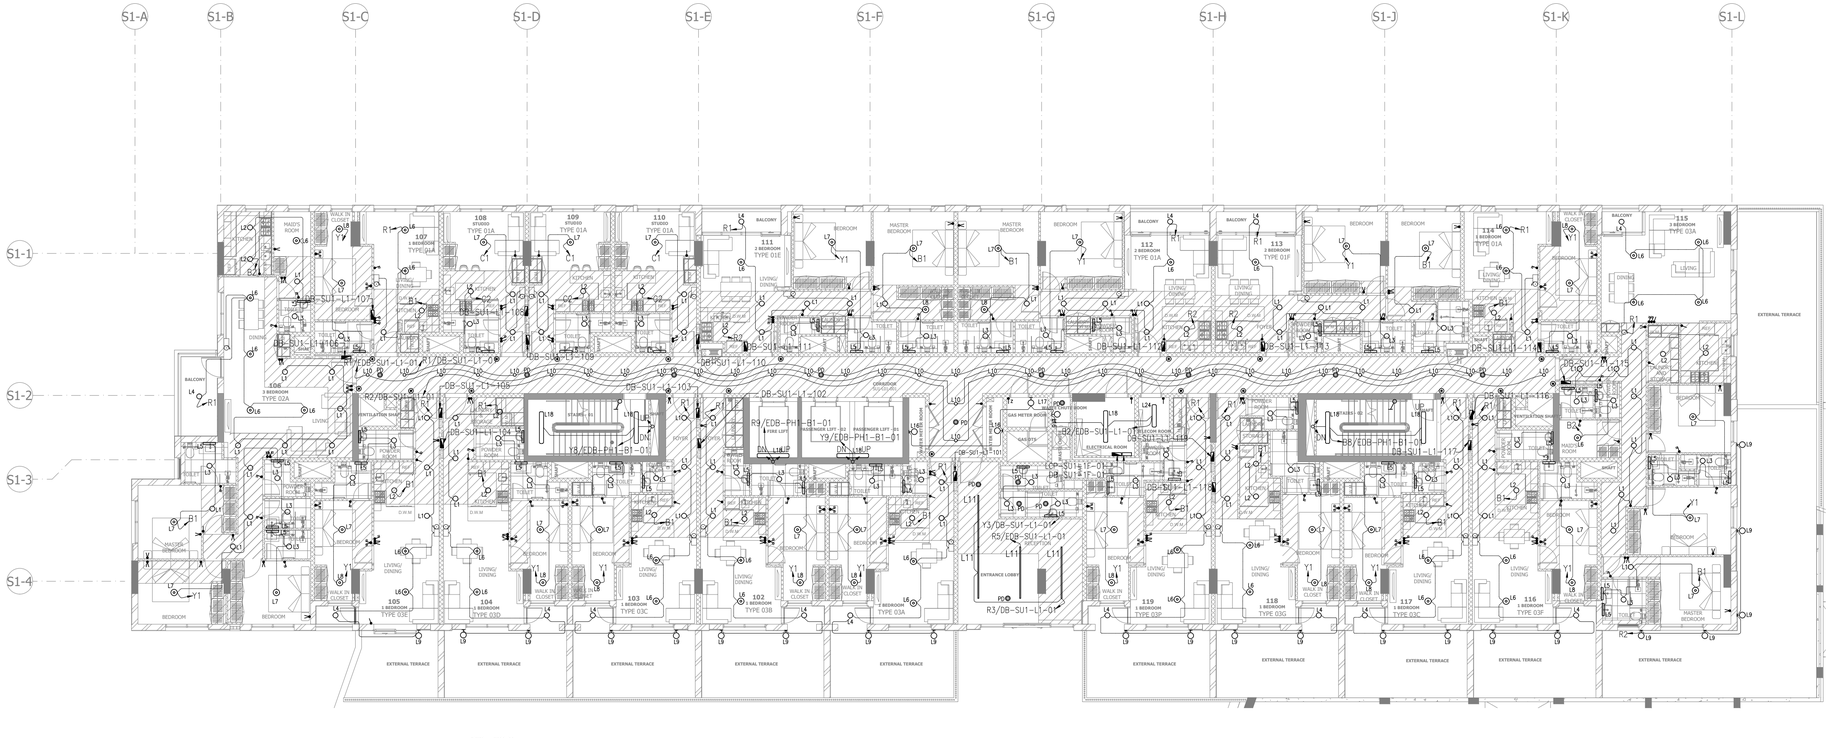



FOR LOCAL AUTHORITY USE ONLY

A1 Original Sheet Size

APPROVAL

CLIENT	ARCHITECTURAL

KEY PLAN

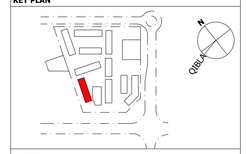

NOTES - GENERAL

1. THIS DRAWING HAS BEEN PRODUCED FOR A PURPOSE AGREED WITH THE CLIENT FOR THE PROJECT AS SHOWN HEREIN. COPIES OR MODIFICATIONS REQUIRE PRIOR CONSENT. IT IS NOT INTENDED TO BE USED BY ANY OTHER PERSON OR FOR ANY OTHER PURPOSE AND ALEF, ITS SUBSIDIARIES, AFFILIATES AND PERMITTED ASSIGNEES ACCEPT NO LIABILITY WHATSOEVER FOR ANY SUCH USE.
2. DIMENSIONS ARE NOT TO BE SCALED FROM THIS DRAWING.
3. ALL DIMENSIONS ARE IN MILLIMETRES AND LEVELS IN METRES UNLESS NOTED OTHERWISE.
4. ANY DISCREPANCIES, EITHER BETWEEN WRITTEN DIMENSIONS AND SITE DIMENSIONS OR WITHIN THESE DRAWINGS SHOULD BE BROUGHT TO THE IMMEDIATE ATTENTION OF THE RESPECTIVE CONSULTANT BEFORE EXECUTING THE WORKS.
5. THIS DRAWING IS TO BE READ IN CONJUNCTION WITH ALL OTHER DOCUMENTATION FORMING THE CONSTRUCTION CONTRACT.
6. ALL EXISTING DIMENSIONS/ LEVELS ETC. INDICATED ON DRAWINGS ARE TO BE VERIFIED ON SITE.
7. CONTRACTOR TO SUBMIT COORDINATED SHOP DRAWINGS FOR RESPECTIVE CONSULTANT'S APPROVAL AS REQUIRED PRIOR TO COMMENCEMENT OF WORKS AT SITE.
8. ALL LEVELS ARE TO LOCAL MUNICIPALITY DATUM (SMD).

GENERAL ANNOTATION

FFL	FINISHED FLOOR LEVEL	NGL	NATURAL GROUND LEVEL
SSL	STRUCTURAL SLAB LEVEL	LVL	LEVEL
TOW	TOP OF WALL	TOK	TOP OF KERB
TOP	TOP OF PARAPET	TOR	TOP OF ROOF

NOTES

1. FOR LEGENDS ABBREVIATIONS AND GENERAL NOTES REFER TO DRAWING NO.EGE-0003, EGE-0004, EGE-0005 & EGE-0006.
2. THIS DRAWING SHALL BE READ IN CONJUNCTION WITH CONTRACT DOCUMENTS, SPECIFICATIONS, LAYOUT DRAWINGS, AND OTHER RELEVANT DRAWINGS FOR COORDINATION.
3. THE FINAL SETTING OUT OF THE FIXTURES SHALL BE IN COORDINATION WITH THE OTHER SERVICES AND APPROVED RCP.
4. GROUPING OF THE LIGHTING CIRCUITS SHALL BE ARRANGED TO MEET THE FINAL APPROVED LIGHTING CONTROL STRATEGY.
5. COMPLETE LIGHTING LUX CALCULATION SHALL BE SUBMITTED FOR ENGINEERS REVIEW WITH THE APPROVED SELECTED FIXTURES.
7. ALL LIGHT FIXTURE SELECTION SHALL BE MADE IN CONCURRENCE WITH THE SMART HOME SYSTEM APPROVED FINAL.
8. DOOR BELL SOUNDERS (WITHIN THE APARTMENTS) TO BE ALLOCATED ABOVE THE CEILING (I.E. LIVING ROOM PREFERABLY OR KITCHEN AREA). THESE SHALL NOT BE EXPOSED VISUALLY INSIDE THE APARTMENTS. SUBMIT DETAILS FOR CLIENT APPROVAL.
9. SWITCHES AND SENSORS SHALL BE PROVIDED TO MEET THE LIGHTING CONTROL STRATEGY.
10. APARTMENTS EXCEPT STUDIOS ARE TO BE PROVIDED WITH SMART HOME SYSTEM. SWITCHES SHOWN INSIDE THE APARTMENT LIGHTING LAYOUT SHALL BE CONSIDERED FOR SWITCHING GUIDANCE ONLY.
11. ALL THE SWITCHES AND LOCATION SHALL BE AS PER FINAL APPROVED SMART HOME SYSTEM.

REVISION	DESCRIPTION	DATE	BY
00	ISSUED FOR CONSTRUCTION	AUG 2023	MIMAR
T3	TENDER ADDENDUM	MAY 2023	MIMAR

OWNER

Alef

Alef Group, PO Box 998 Sharjah, UAE

www.alefgroup.ae 06-5544111

CONSULTANT

MIMAR ARCHITECTURE + ENGINEERING

MIMAR EMIRATES ENGINEERING CONSULTANTS

P.O. BOX 26004, SHARJAH,U.A.E. | Tel: +9716 554 0800 | www.mimararchitecture.com

mimar@mimar-group.com

PROJECT

AL MAMSHA SEERAH (PHASE 1):

PROPOSED B+G(PT)+P2+9+ROOF, SUROOR 1,2,3,4 RESI. & COMMERCIAL BUILDGS, ON PLOT NO: MUK NO. 2/3114. GOV NO. 7463. MOWEILAH COMMERCIAL, SHARJAH.

DRAWING TITLE

SUROOR-01
LEVEL 01 FLOOR PLAN
LIGHTING LAYOUT

DRAWN	-	CHECKED	-	APPROVED	-
SCALE	1 : 150	DATE	AUG 2023	PROJ. No	S80SHJ22

CLIENT DRAWING No. ALEF-MZ02-SU1-L01-ELG-1000

REVISION 00

MUNICIPALITY DRAWING No. ELG-1000