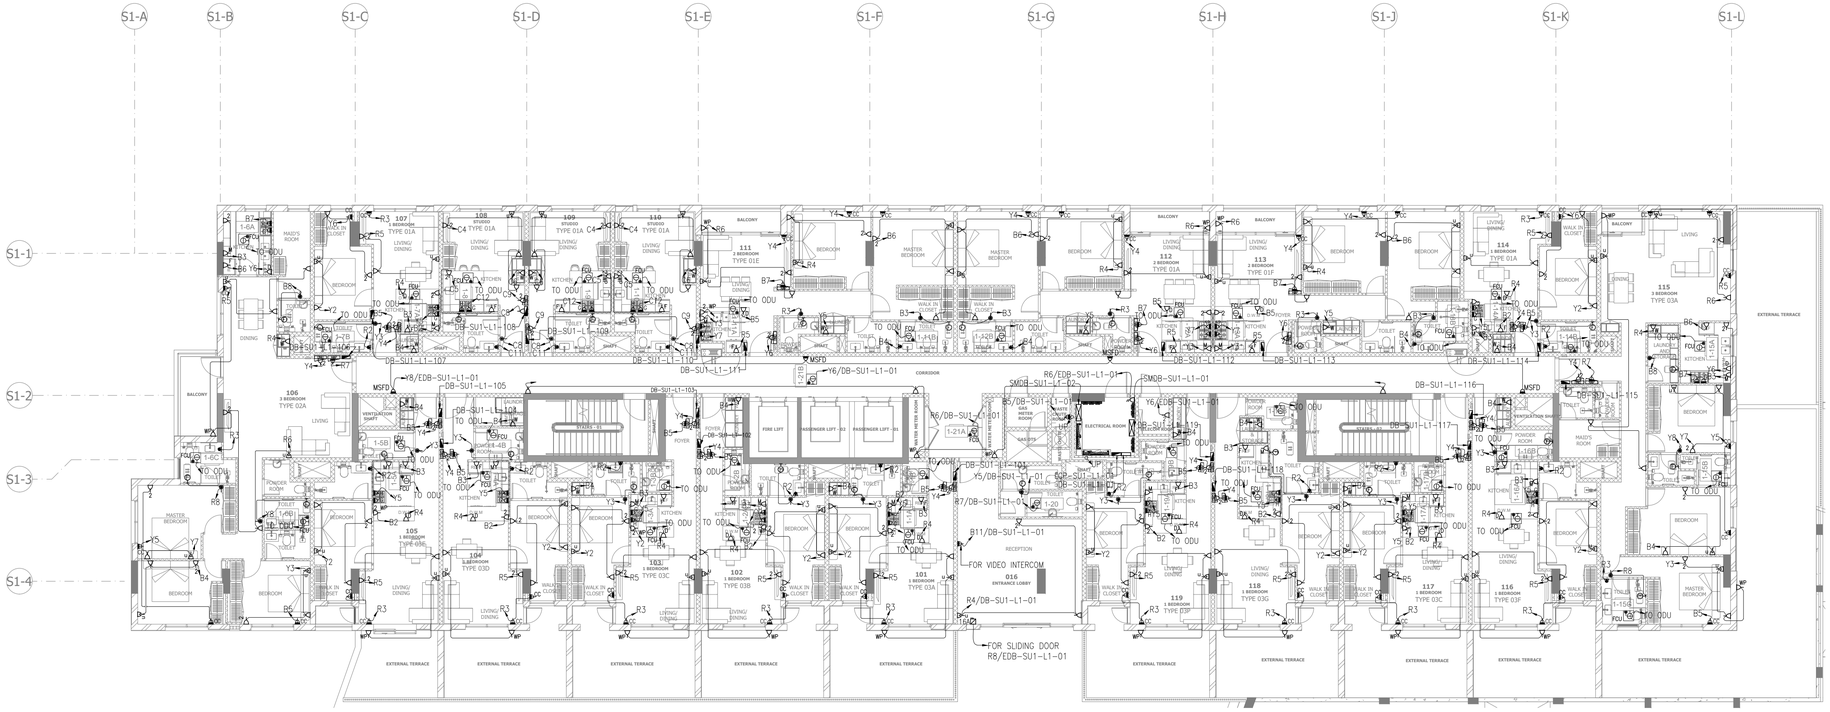


NOTE:-
CONTRACTOR TO INCLUDE PROVISION FOR ENTRANCE PANEL FOR HOME AUTOMATION SYSTEM IN ALL APARTMENT UNIT.

NOTE:-
WASHING MACHINE AND DISHWASHER OUTLETS SHALL BE WEATHER PROOF W/P

NOTE:-
POWER PROVISION CONTAINMENT FOR WAP SHALL BE PROVIDED BY THE CONTRACTOR.

DB NAMING CONVENTION

DB–SU1–L1–101–1B

- BOARD DESIGNATOR
- TOWER DESIGNATOR
- LEVEL DESIGNATOR
- UNIT DESIGNATOR
- ROOM TYPE DESIGNATOR (ST, 1B, 2B, 3B)


FOR LOCAL AUTHORITY USE ONLY

A1 Original Sheet Size

APPROVAL

CLIENT	ARCHITECTURAL

KEY PLAN

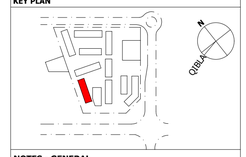

NOTES - GENERAL

1. THIS DRAWING HAS BEEN PRODUCED FOR A PURPOSE AGREED WITH THE CLIENT FOR THE PROJECT AS SHOWN HEREIN. COPIES OR MODIFICATIONS REQUIRE PRIOR CONSENT. IT IS NOT INTENDED TO BE USED BY ANY OTHER PERSON OR FOR ANY OTHER PURPOSE AND ALEF, ITS SUBSIDIARIES, AFFILIATES AND PERMITTED ASSIGNEES ACCEPT NO LIABILITY WHATSOEVER FOR ANY SUCH USE.
2. DIMENSIONS ARE NOT TO BE SCALED FROM THIS DRAWING.
3. ALL DIMENSIONS ARE IN MILLIMETRES AND LEVELS IN METRES UNLESS NOTED OTHERWISE.
4. ANY DISCREPANCIES, EITHER BETWEEN WRITTEN DIMENSIONS AND SITE DIMENSIONS OR WITHIN THESE DRAWINGS SHOULD BE BROUGHT TO THE IMMEDIATE ATTENTION OF THE RESPECTIVE CONSULTANT BEFORE EXECUTING THE WORKS.
5. THIS DRAWING IS TO BE READ IN CONJUNCTION WITH ALL OTHER DOCUMENTATION FORMING THE CONSTRUCTION CONTRACT.
6. ALL EXISTING DIMENSIONS/ LEVELS ETC. INDICATED ON DRAWINGS ARE TO BE VERIFIED ON SITE.
7. CONTRACTOR TO SUBMIT COORDINATED SHOP DRAWINGS FOR RESPECTIVE CONSULTANT'S APPROVAL AS REQUIRED PRIOR TO COMMENCEMENT OF WORKS AT SITE.
8. ALL LEVELS ARE TO LOCAL MUNICIPALITY DATUM (SMD).

GENERAL ANNOTATION

FFL	FINISHED FLOOR LEVEL	NGL	NATURAL GROUND LEVEL
SSL	STRUCTURAL SLAB LEVEL	LVL	LEVEL
TOW	TOP OF WALL	TOK	TOP OF KERB
TOP	TOP OF PARAPET	TOR	TOP OF ROOF

NOTES

1. FOR LEGENDS ABBREVIATIONS AND GENERAL NOTES REFER TO DRAWING NO.EGE-0003, EGE-0004, EGE-0005 & EGE-0006.
2. THIS DRAWING SHALL BE READ IN CONJUNCTION WITH CONTRACT DOCUMENTS, SPECIFICATIONS, LAYOUT DRAWINGS, AND OTHER RELEVANT DRAWINGS FOR COORDINATION.
3. LOCATION OF ALEF LOGO SHOWN IS INDICATIVE ONLY. CONTRACTOR TO COORDINATE WITH FINAL VENDOR FOR ALL REQUIREMENTS.
4. ALL ISOLATOR FOR LIFE SAFETY EQUIPMENT SHALL BE FIRE RATED.
5. STARTING EQUIPMENT FOR ALL MOTORS SHALL BE AS PER FINAL SELECTION OF EQUIPMENT.
6. ALL CABLE TRAYS SHALL BE PROVIDED WITH SUN SHADE COVER.
7. GENERAL PURPOSE SOCKET OUTLET SHOWN ARE INDICATIVE ONLY LOCATION SHALL BE FINALIZED BASED ON THE EASE OF MAINTENANCE AND FINAL LOCATION OF EQUIPMENT ON ROOF.
8. WIRING FOR THE APARTMENT AC UNITS SHALL BE VIA DEDICATED CONDUITS FROM THE RESPECTIVE UNIT DB'S. REFER DETAIL-5 ON DRAWING EDT-5003.
9. CONTRACTOR SHALL ENSURE THE MINIMUM MAINTENANCE CLARENCE IS CONSIDERED FOR ALL INSTALLATIONS.
10. WHEREVER CONTAINMENT IS NOT INDICATED, CONTRACTOR SHALL PROVIDE THE CONTAINMENT FOR ALL EQUIPMENT.

REVISION	DESCRIPTION	DATE	BY
00	ISSUED FOR CONSTRUCTION	AUG 2023	MIMAR
T1	TENDER ADDENDUM	MAY 2023	MIMAR

OWNER

Alef

Alef Group, PO Box 998 Sharjah, UAE

www.alefgroup.ae (6)(5941111)

CONSULTANT

MIMAR ARCHITECTURE + ENGINEERING

MIMAR EMIRATES ENGINEERING CONSULTANTS

P.O. BOX 23004, SHARJAH-U.A.E. | Tel: +0776 554 9922 | www.mimararchitects.com

PROJECT

AL MAMSHA SEERAH (PHASE 1):

PROPOSED B+G(P1)+P2+9+ROOF.
SUROOR 1,2,3,4 RESI. & COMMERCIAL BUILDGS,
ON PLOT NO: MULK NO. 2/3114. GOV NO. 7463.
MOWEILAH COMMERCIAL, SHARJAH.

DRAWING TITLE

SUROOR-01
LEVEL 01 FLOOR PLAN
SMALL POWER LAYOUT

DRAWN	-	CHECKED	-	APPROVED	-
SCALE	1 : 150	DATE	AUG 2023	PROJ. No	580SHJ22

CLIENT DRAWING No. ALEF-MZ02-SU1-L01-EPR-1000

REVISION 00

MUNICIPALITY DRAWING No. EPR-1000